


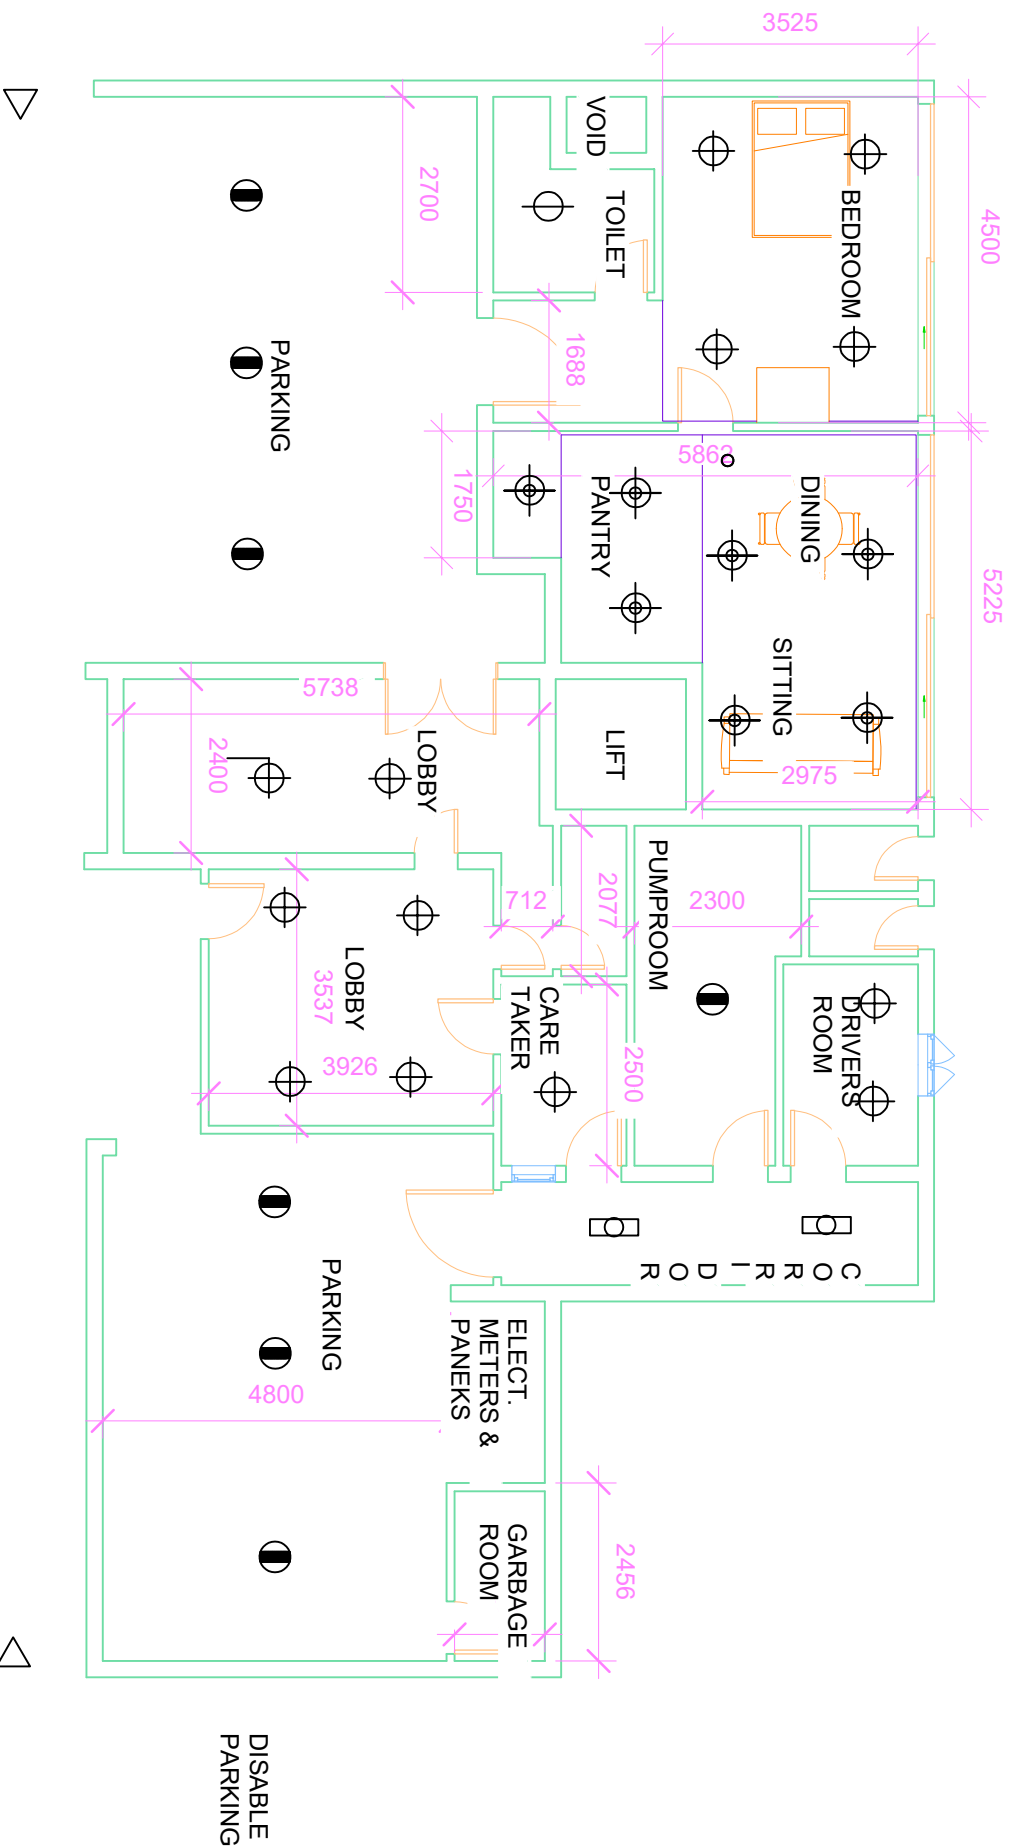

Project

NO. 301,
Rajamawatha,
Anuradhapura.

Legend

- Coreline Slim Downlight
- Coreline Slim Downlight
- Coreline Downlight
- Coreline wall mounted
- SmartBright Direct Panel
- CoreLine Batten
- CoreLine waterproof
- Ledinaire Floodlight