


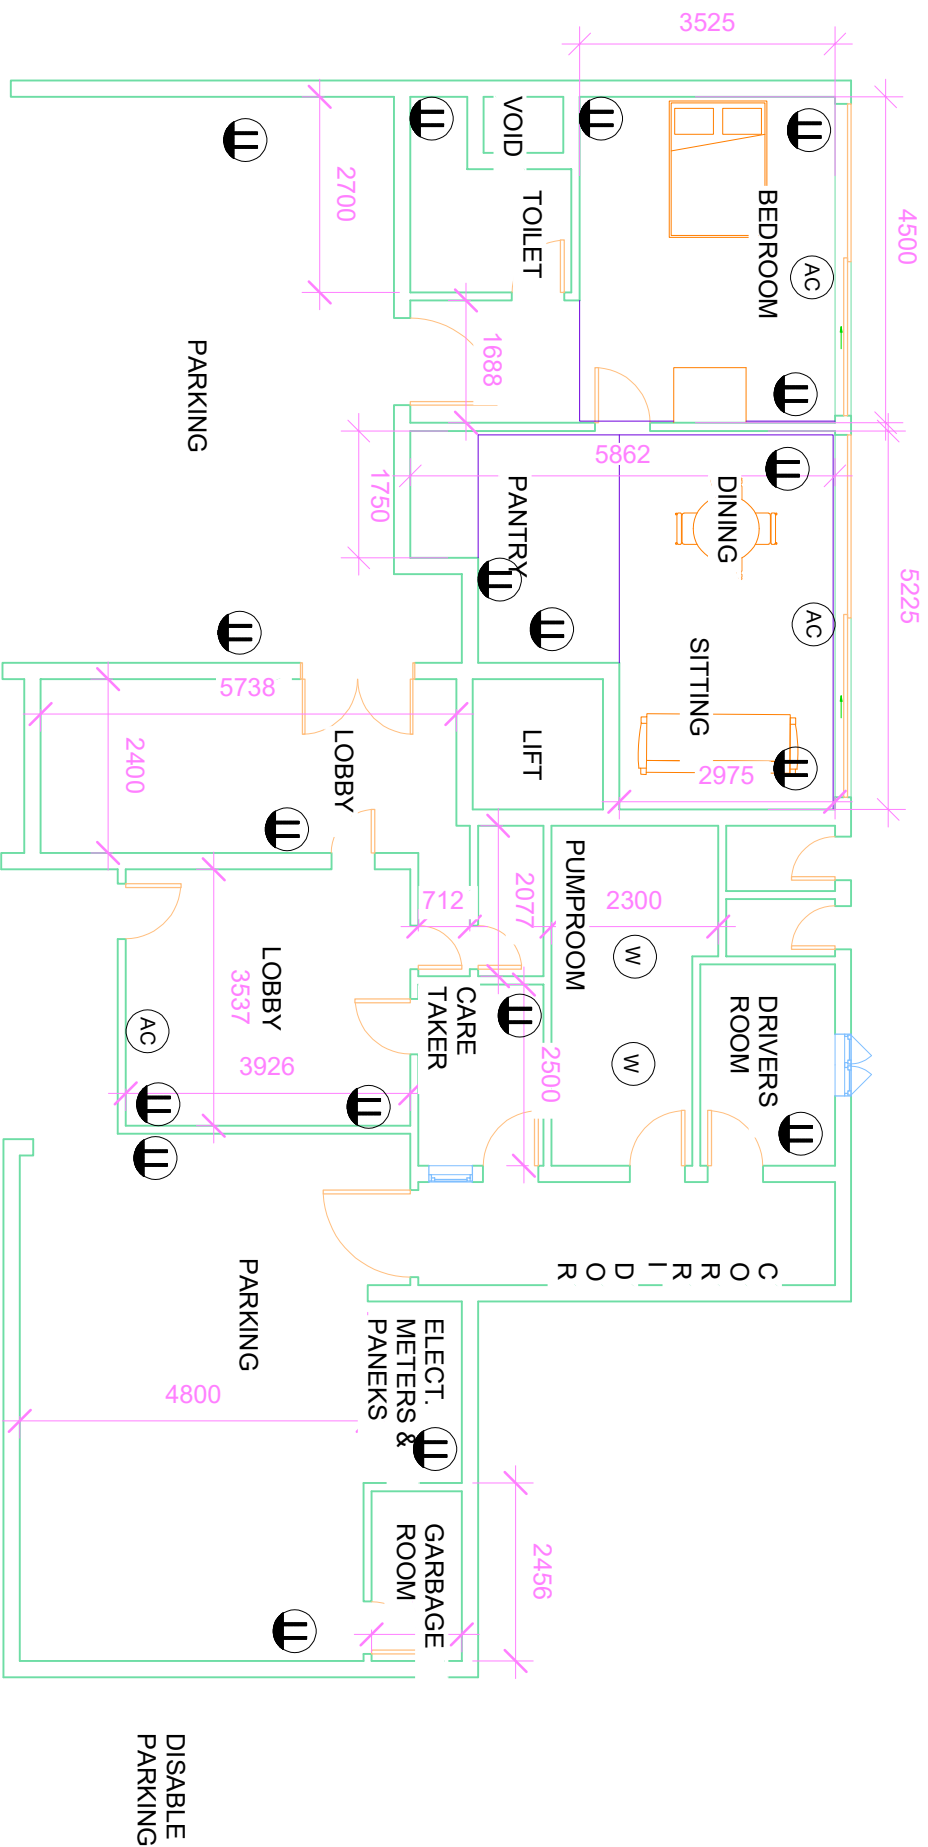

Project NO. 301, Rajamawatha, Anuradhapura.	Legend II Socket outlet AC Air condition W Pump
---	--