


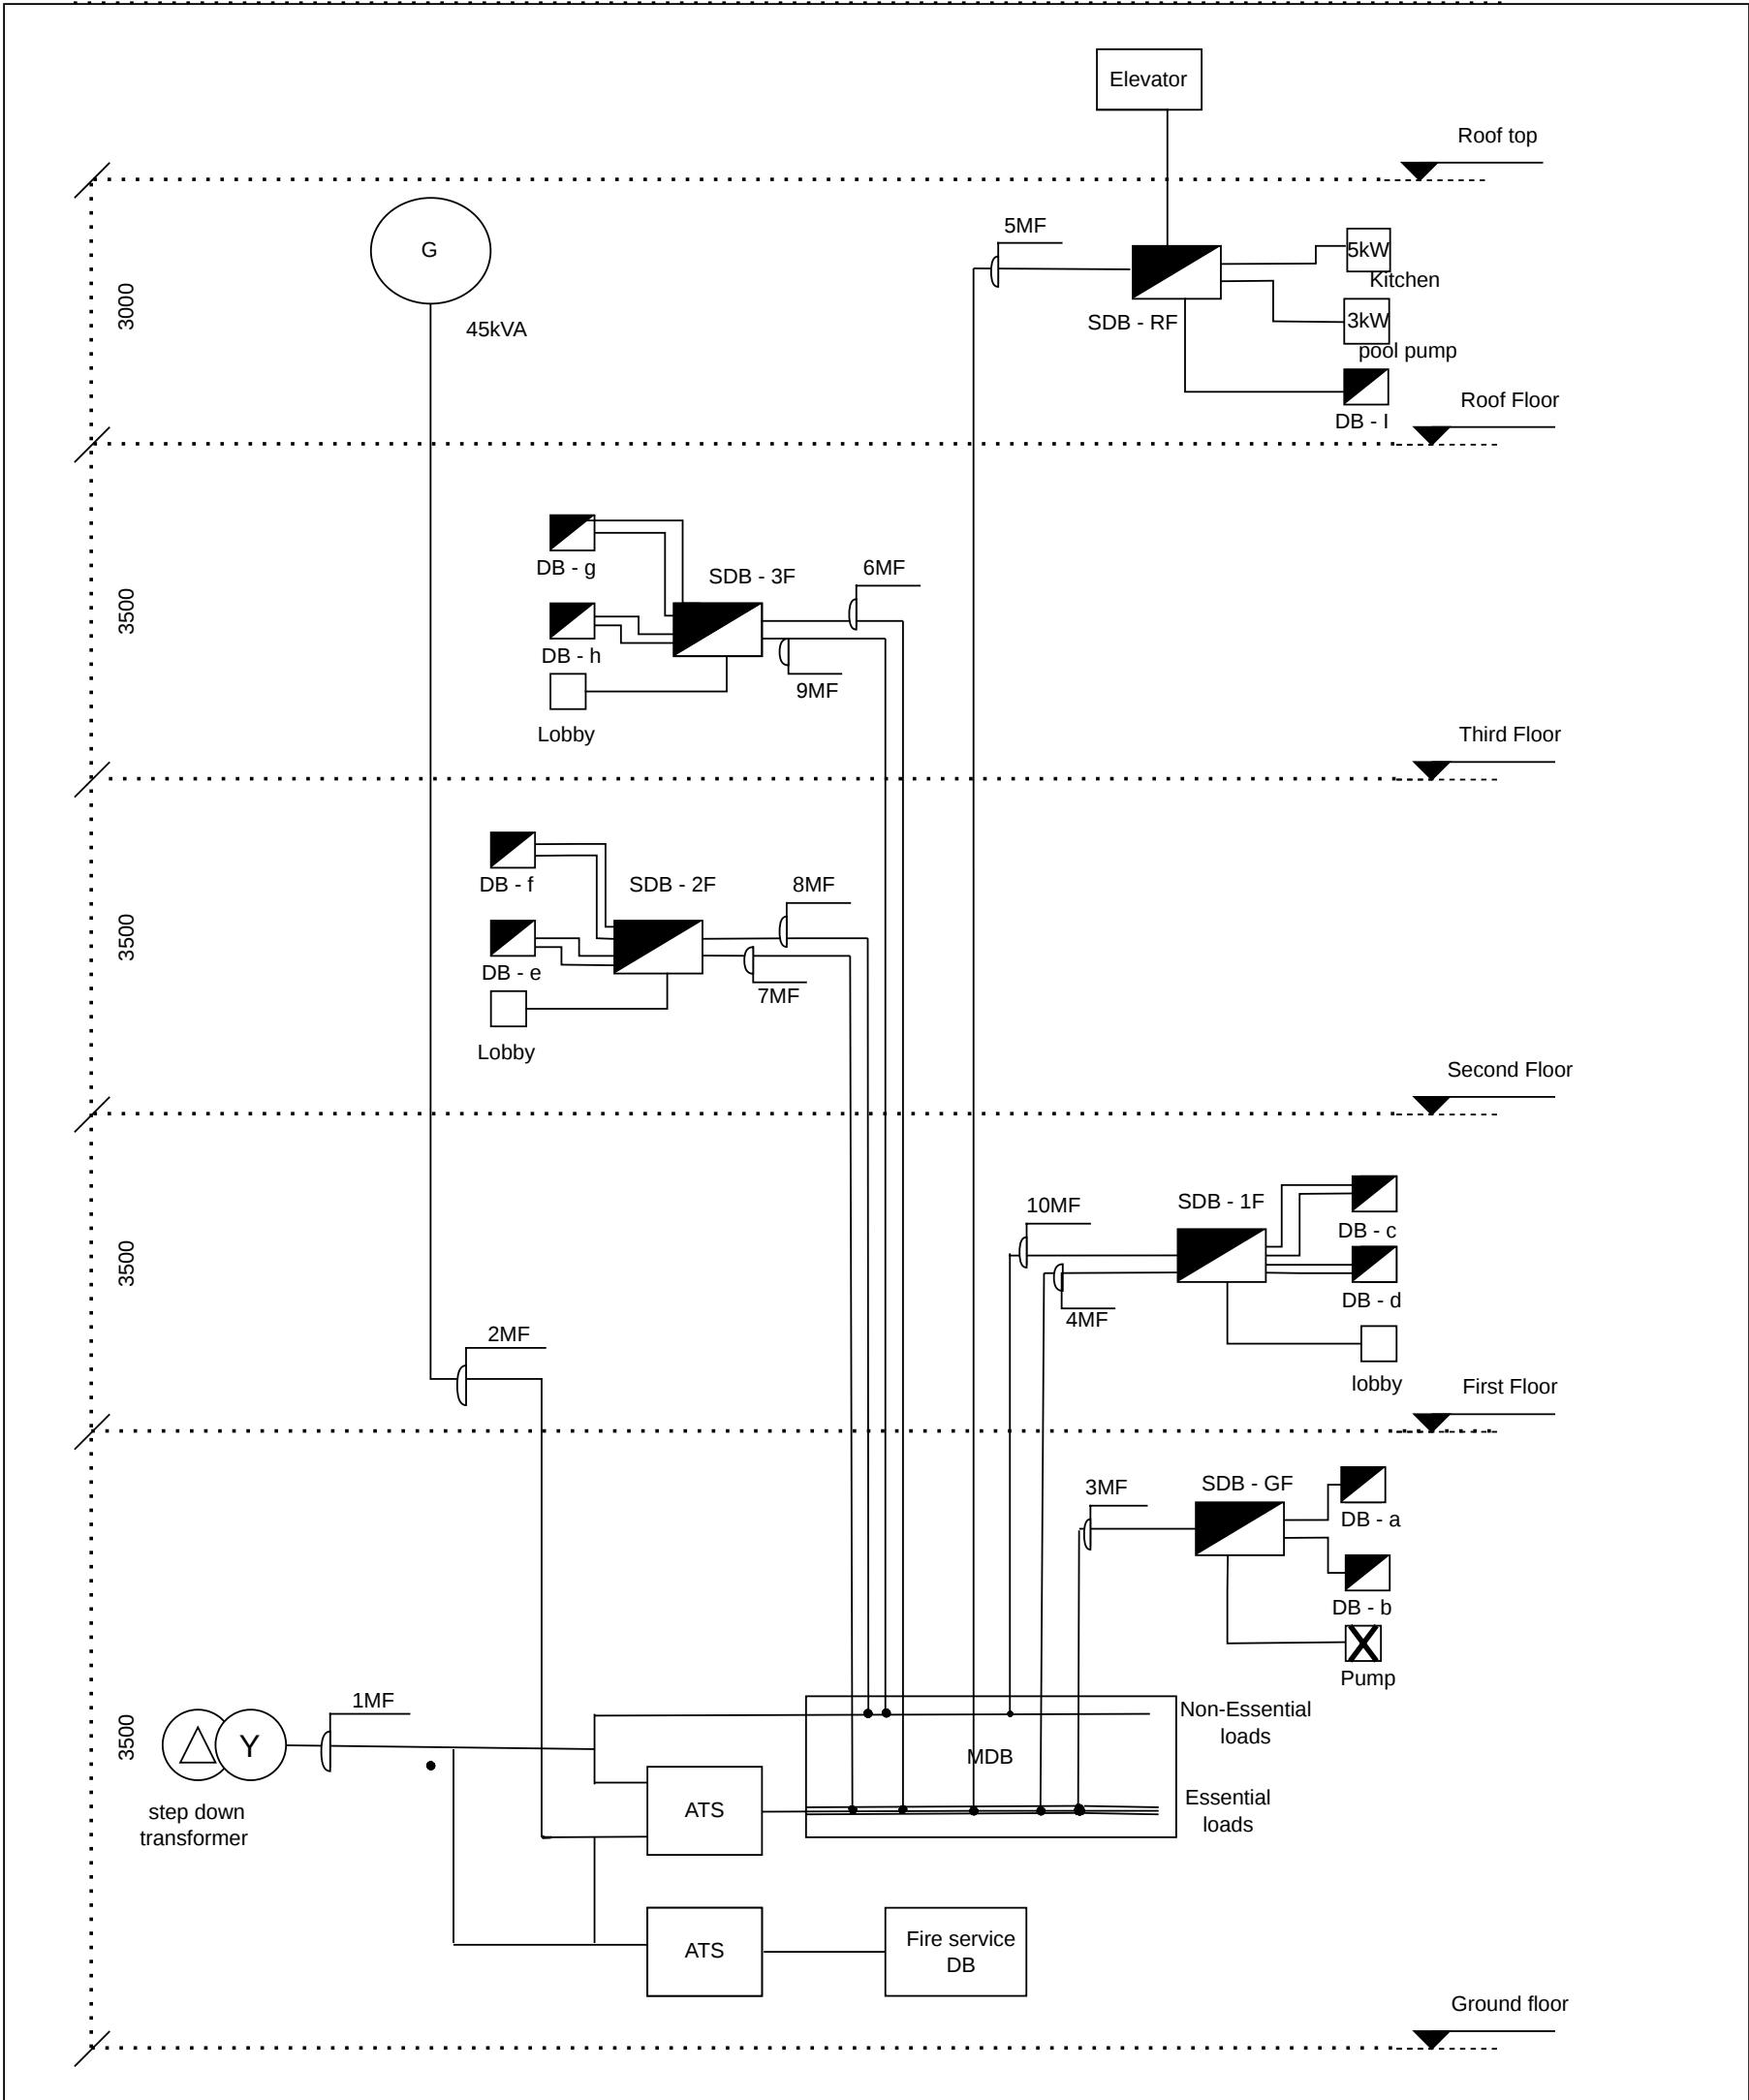

Project No .301, Raja mawatha, Anuradhapura.	Drawing title - LV distribution Shematic diagram	Legend  - Distribution Board  - Transformer  - Generator	Abbreviations - DB - Distribution Board - SDB - Sub distribution board - MDB - Main distribution board - ATS - Automatic transfer switch
---	---	--	---