



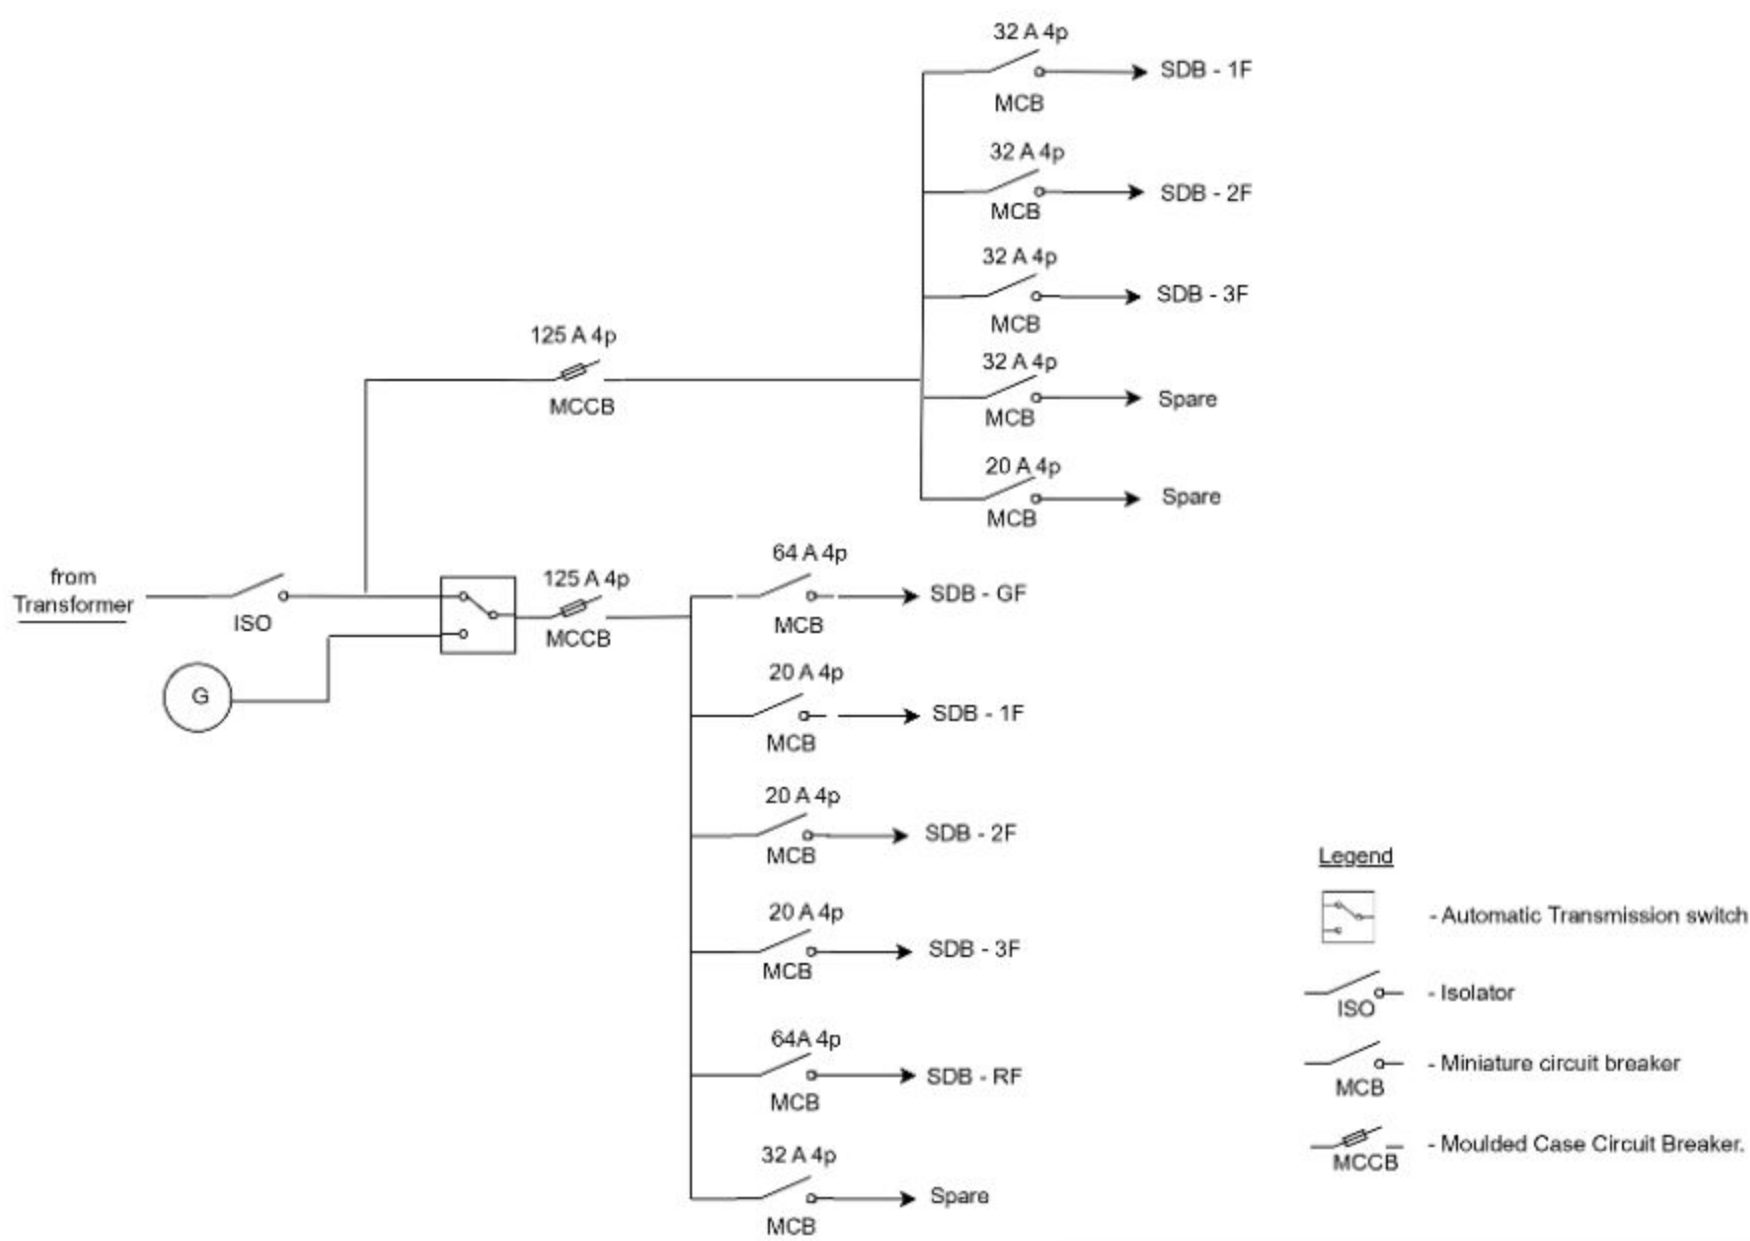


Project	SINGLE LINE DIAGRAM		REVISIONS		
NO.301, Rajamawatah , Anuradhapura.	PROJECT	Apartment Building – Main distribution Board	REV.	DATE	DESCRIPTION
	CLIENT	Mr.ABC xxxxx	0	05/26/2026	Initial issue
	JOB SCOPE	Electrical single line diagram			

PROFESSIONAL STATEMENT: TO THE BEST OF THE CONTRACTOR'S KNOWLEDGE THESE PLANS COMPLY WITH THE RELEVANT CODES AND STANDARDS REQUIRED BY THE AUTHORITY HAVING JURISDICTION.

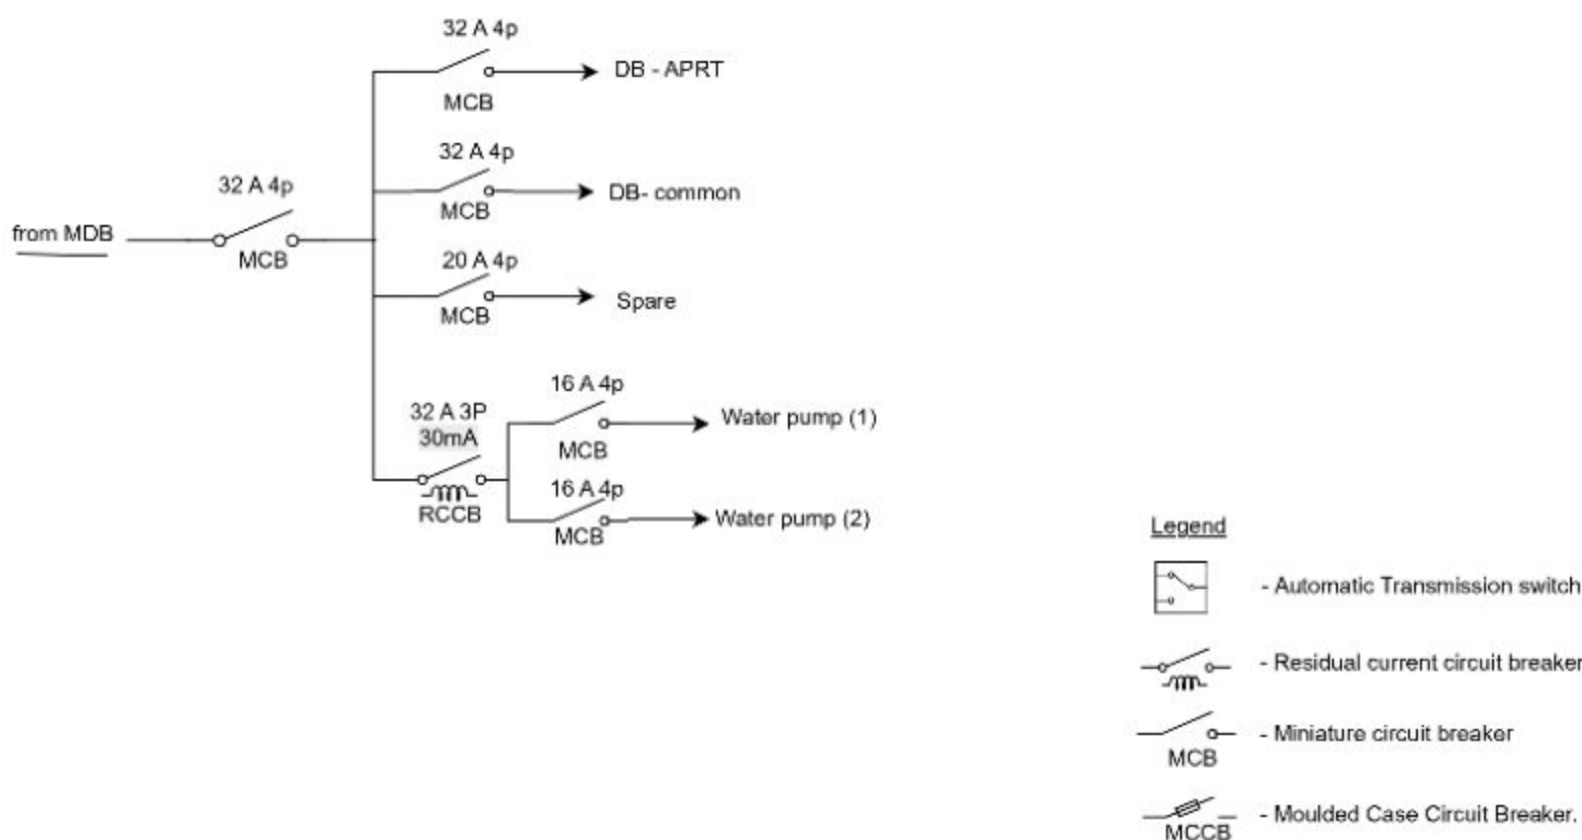


Project	SINGLE LINE DIAGRAM		REVISIONS		
NO.301, Rajamawatah , Anuradhapura.	PROJECT	Apartment Building – Sub distribution Board	REV.	DATE	DESCRIPTION
	CLIENT	Mr.ABC xxxxx	0	05/26/2026	Initial issue
	JOB SCOPE	Electrical single line diagram			

PROFESSIONAL STATEMENT: TO THE BEST OF THE CONTRACTOR'S KNOWLEDGE THESE PLANS COMPLY WITH THE RELEVANT CODES AND STANDARDS REQUIRED BY THE AUTHORITY HAVING JURISDICTION.

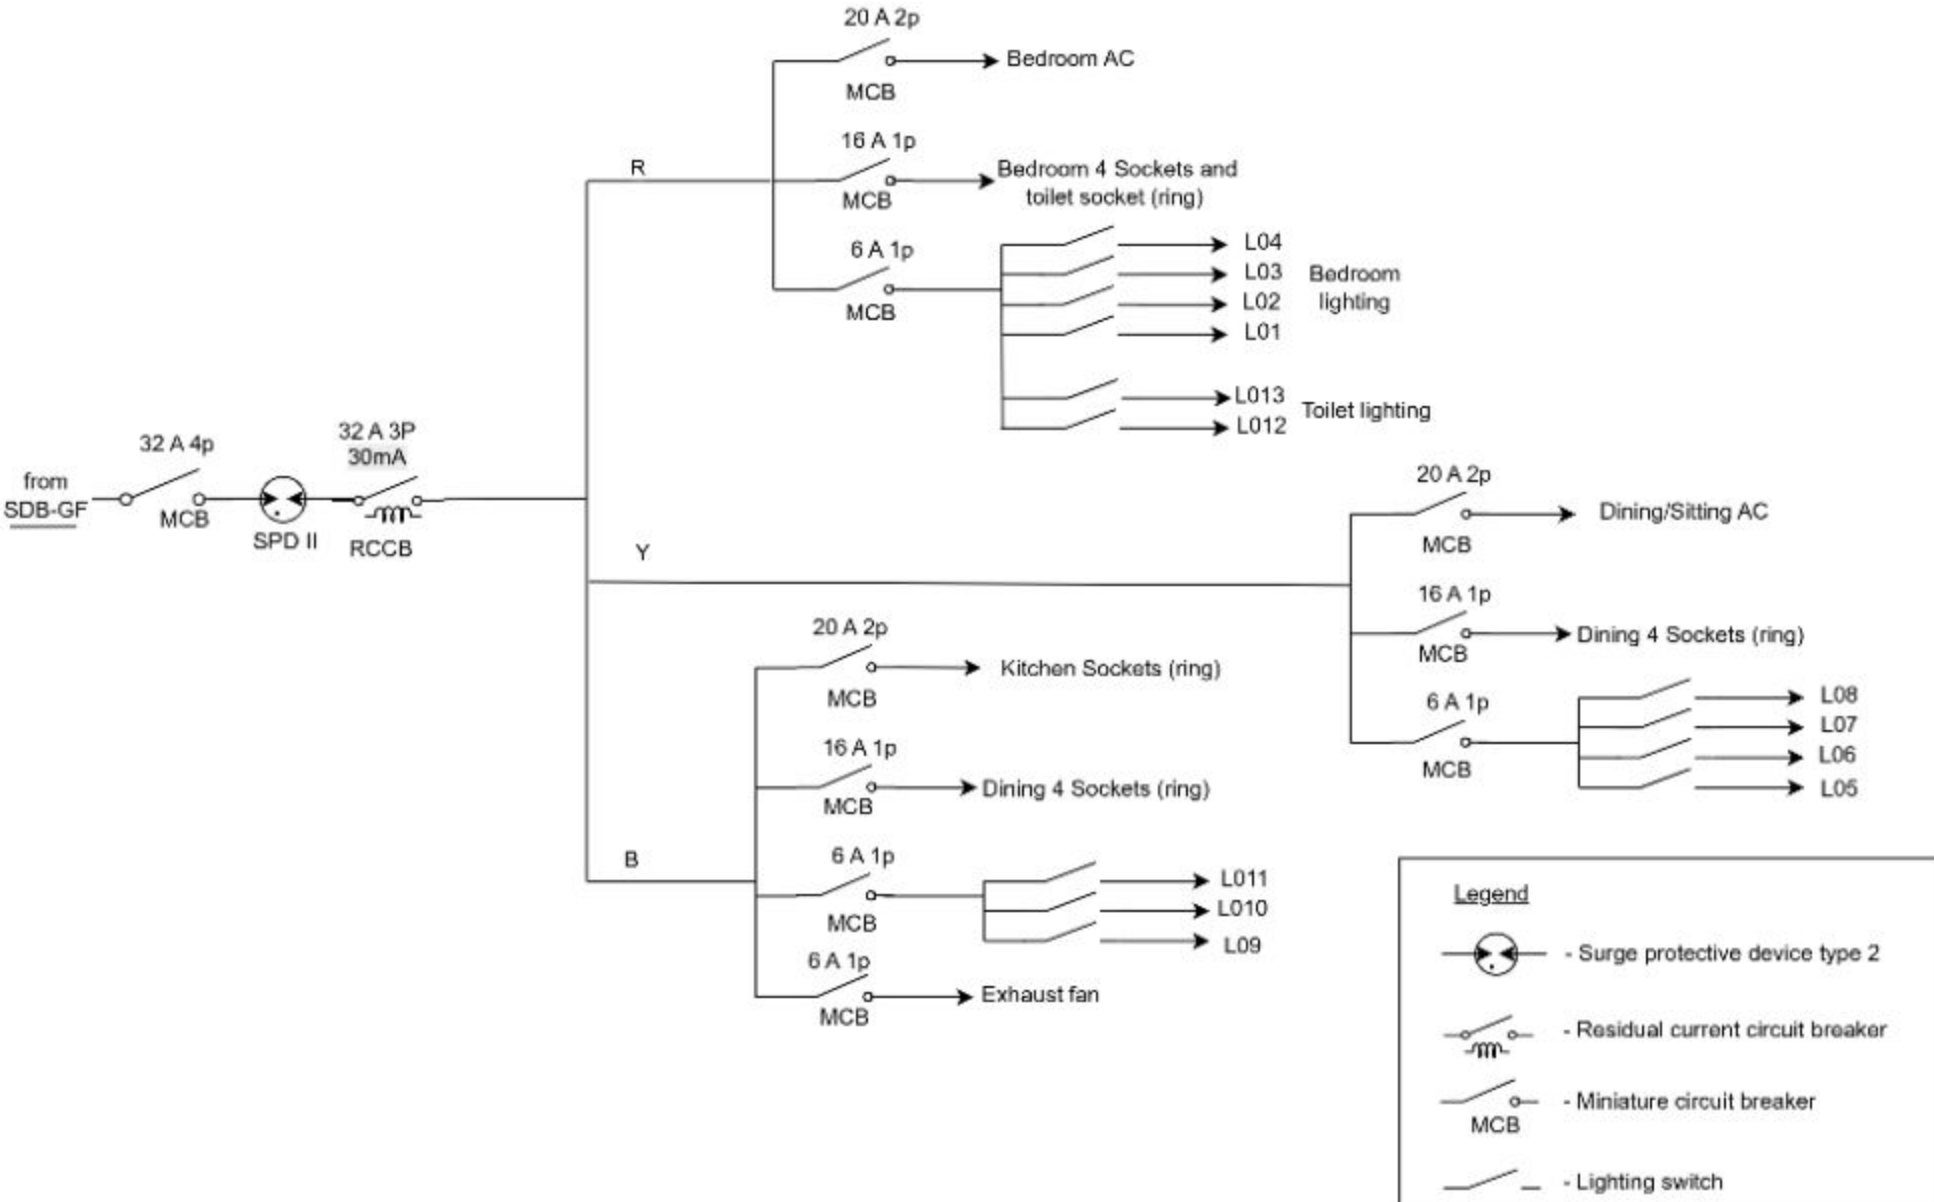


Project	SINGLE LINE DIAGRAM		REVISIONS		
NO.301, Rajamawatah , Anuradhapura.	PROJECT	Apartment Building – Distribution Board (APRT)	REV.	DATE	DESCRIPTION
	CLIENT	Mr.ABC xxxxx	0	05/26/2026	Initial issue
	JOB SCOPE	Electrical single line diagram			

PROFESSIONAL STATEMENT: TO THE BEST OF THE CONTRACTOR'S KNOWLEDGE THESE PLANS COMPLY WITH THE RELEVANT CODES AND STANDARDS REQUIRED BY THE AUTHORITY HAVING JURISDICTION.

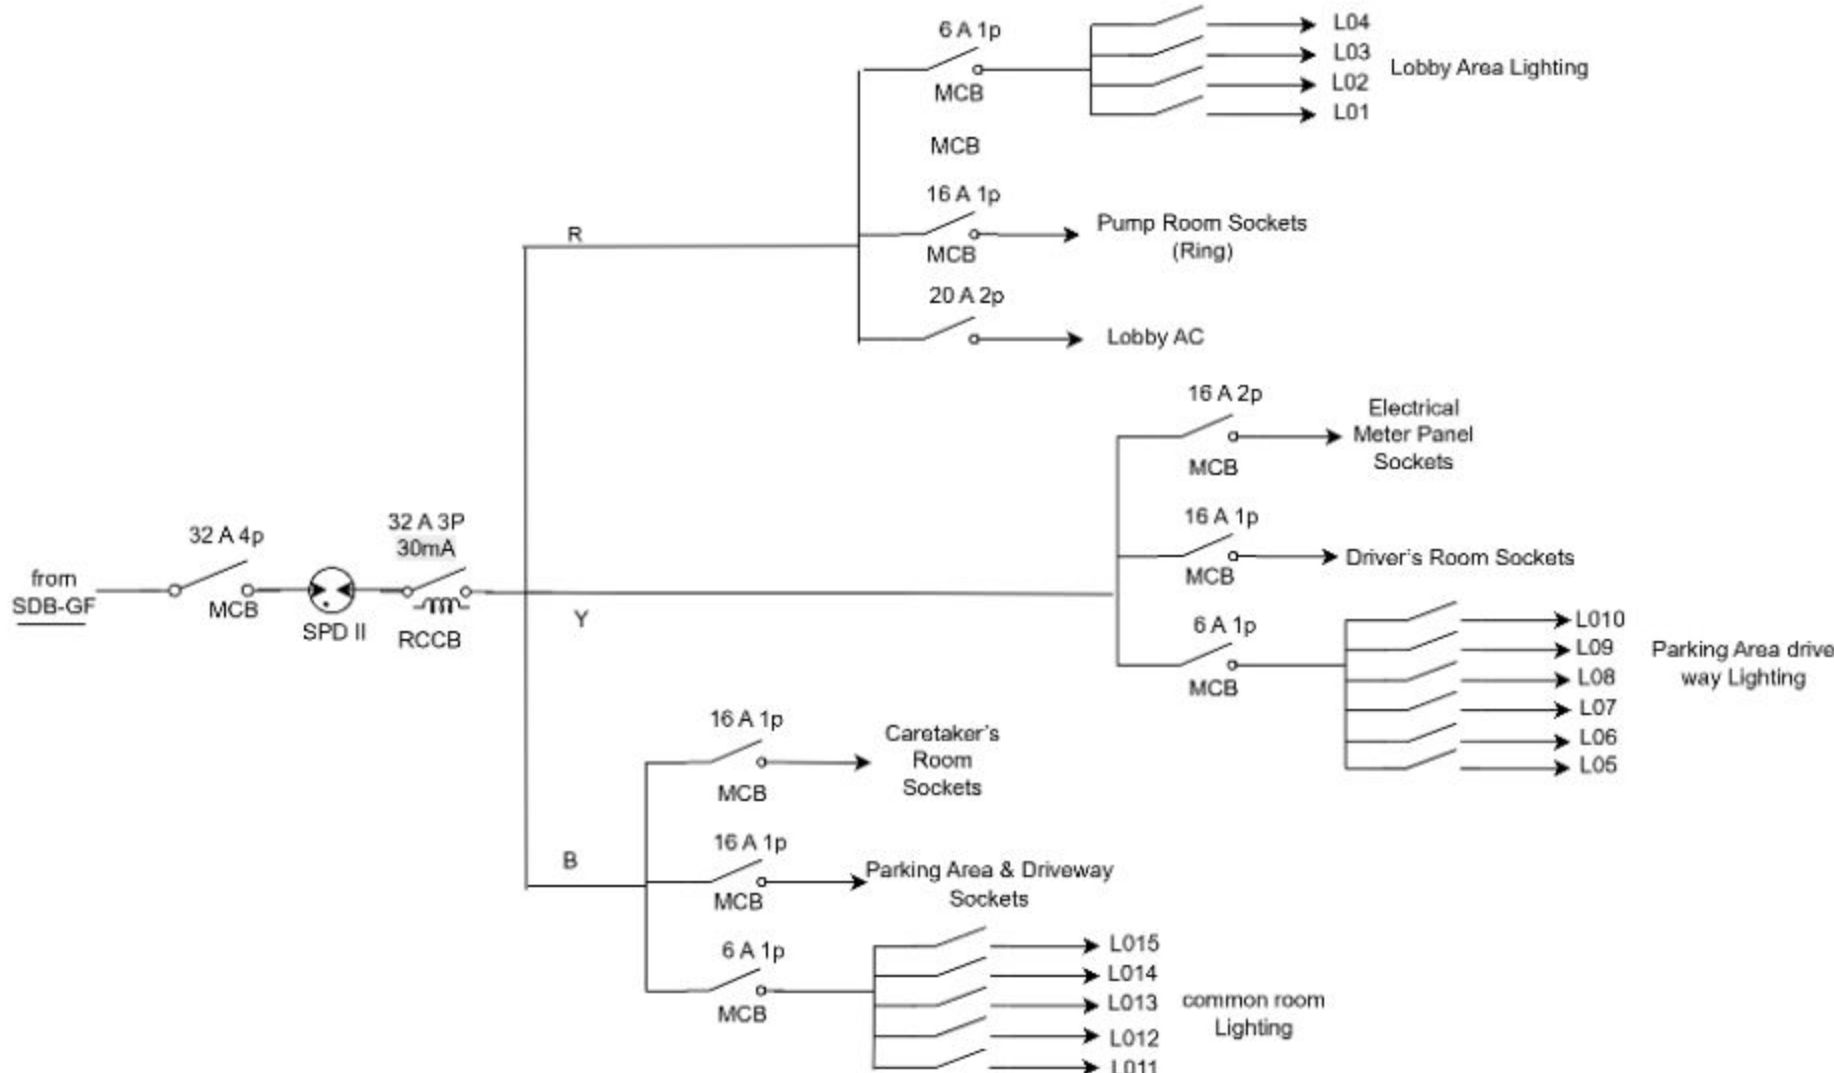

Project	SINGLE LINE DIAGRAM		REVISIONS		
NO.301, Rajamawatah , Anuradhapura.	PROJECT	Apartment Building – Common Distribution Board ground	REV.	DATE	DESCRIPTION
	CLIENT	Mr.ABC xxxxx	0	05/26/2026	Initial issue
	JOB SCOPE	Electrical single line diagram			

PROFESSIONAL STATEMENT: TO THE BEST OF THE CONTRACTOR'S KNOWLEDGE THESE PLANS COMPLY WITH THE RELEVANT CODES AND STANDARDS REQUIRED BY THE AUTHORITY HAVING JURISDICTION.

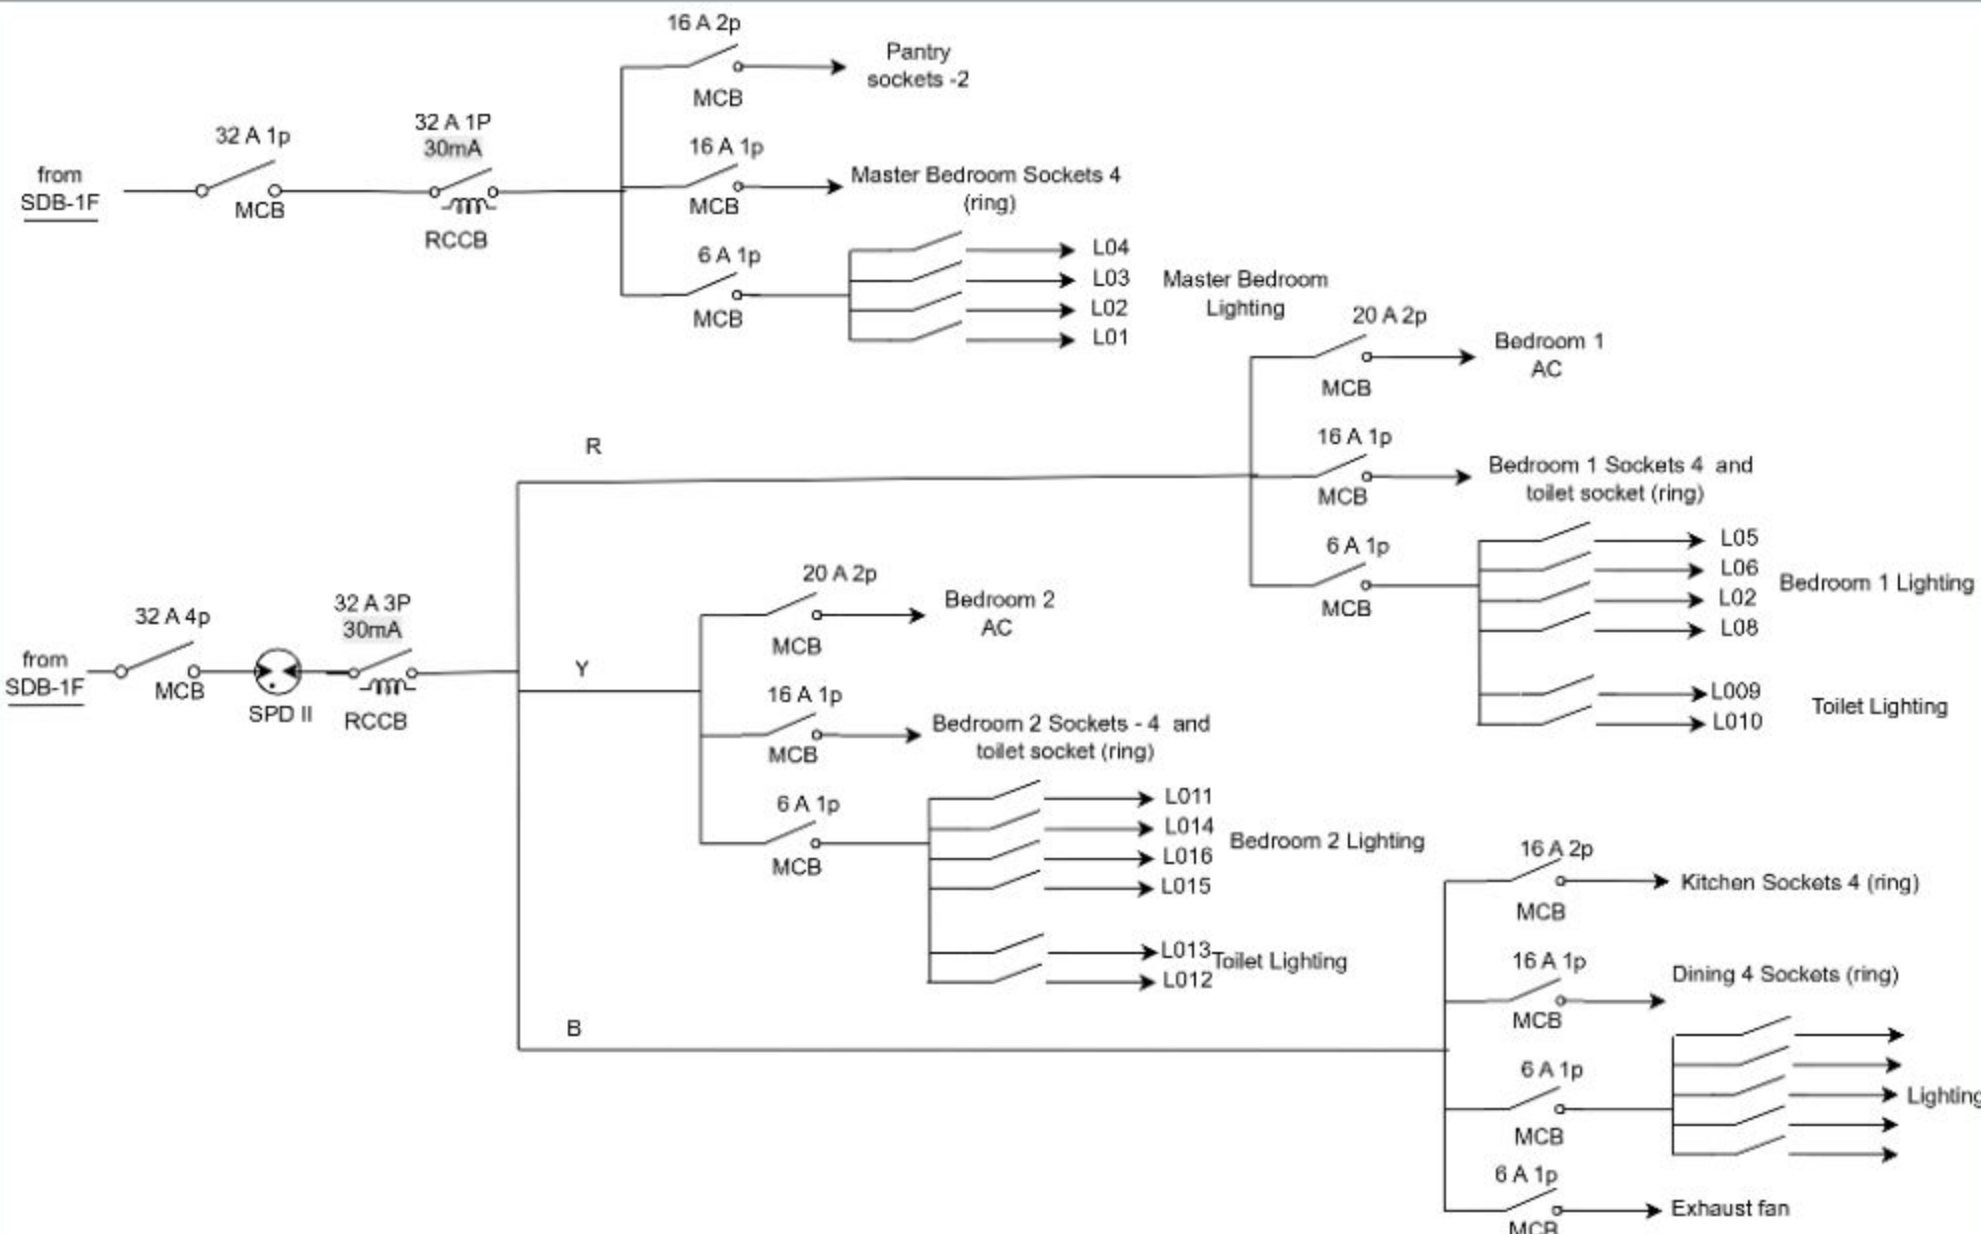

Project	SINGLE LINE DIAGRAM		REVISIONS		
NO.301, Rajamawatah , Anuradhapura.	PROJECT	Apartment distribution board	REV.	DATE	DESCRIPTION
	CLIENT	Mr.ABC xxxxx	0	05/26/2026	Initial issue
	JOB SCOPE	Electrical single line diagram			

PROFESSIONAL STATEMENT: TO THE BEST OF THE CONTRACTOR'S KNOWLEDGE THESE PLANS COMPLY WITH THE RELEVANT CODES AND STANDARDS REQUIRED BY THE AUTHORITY HAVING JURISDICTION.