


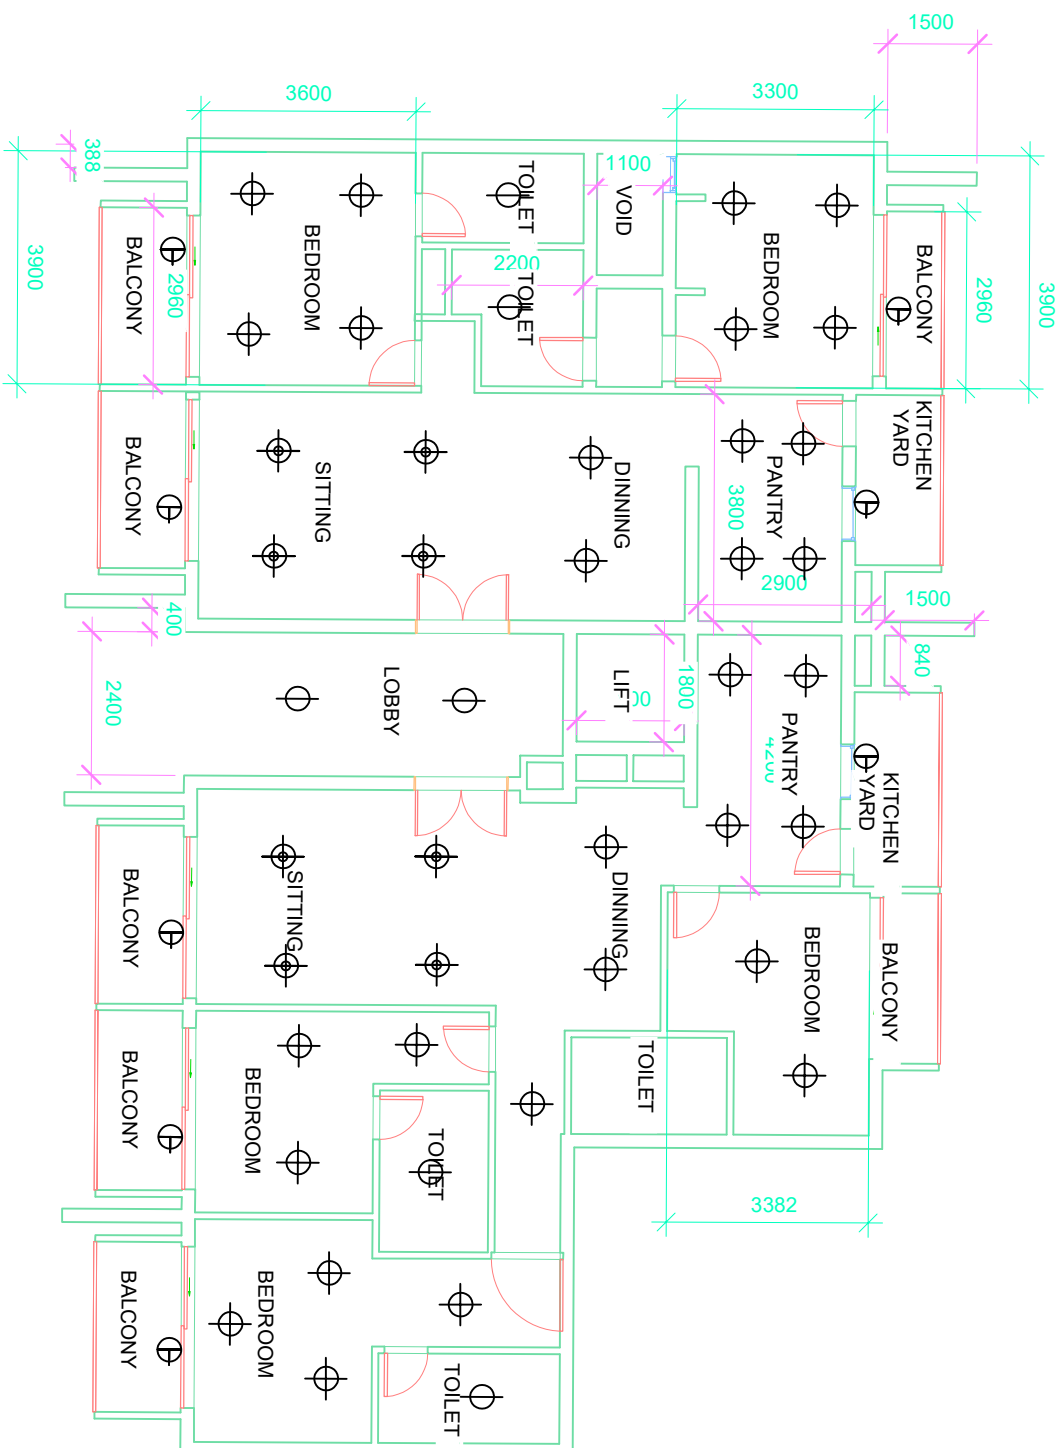

Project	Legend	
NO. 301, Rajamawatha, Anuradhapura.	Coreline Slim Downlight Coreline Slim Downlight Coreline Downlight Coreline wall mounted SmartBright Direct Panel Coreline Batten Coreline waterproof Ledinaire Floodlight	A.M.D.P. Adhikari 2026/05/27